
STATO ATTUALE

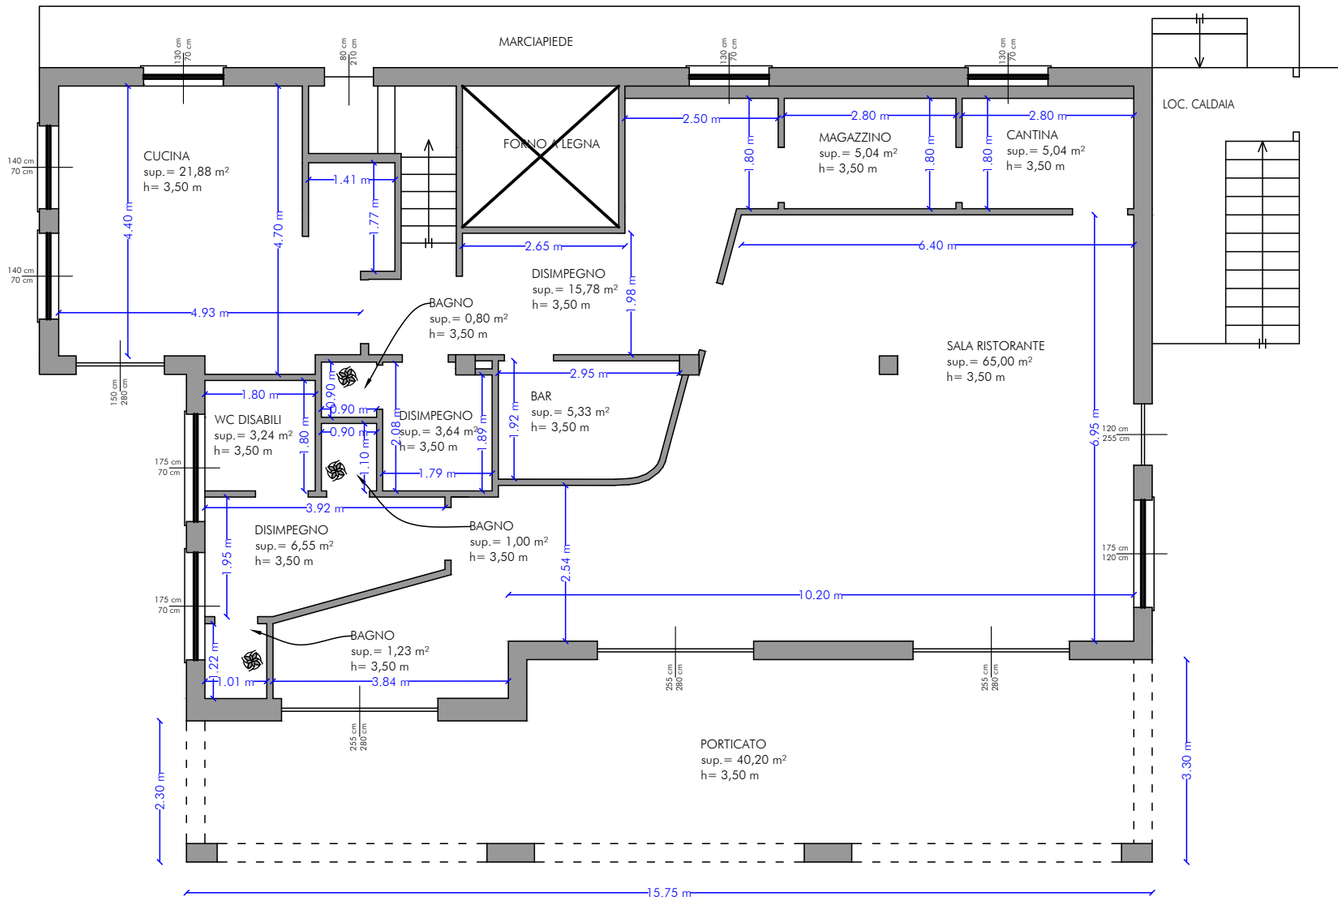

PIANTA PIANO TERRA
scala 1/100

DIMOSTRAZIONE RISPETTO D.M. 05.07.1975					
	Locale	superficie utile locale (mq)	superficie finestrata richiesta (mq)	superficie finestrata esistente (mq)	
STATO ATTUALE	cucina	21,88	2,74	7,07	verificato
	disimpegno	15,78	0	0	verificato
	cantina	5,04	0	0,91	verificato
	magazzino	5,04	0	0	verificato
	wc disabili	3,24	0,10	1,23	verificato
	bagno	0,80	0,10	0	aspirazione forzata
	bagno	1,00	0,13	0	aspirazione forzata
	bar	5,33	0	0	verificato
	disimpegno	3,64	0	0	verificato
	disimpegno	6,55	0	0	verificato
	sala ristorante	65,00	8,13	23,52	verificato
	bagno	1,23	0,15	0	aspirazione forzata
TOTALE SUPERFICIE UTILE (mq)				134,53	

VP6 ENGINEERING

Via Roma n.14 - 17024 Finale Ligure (SV)
tel. 019.69.20.52 - fax 019.68.98.677
P.IVA: 0 1 7 9 3 4 6 0 0 9 6
e-mail: info@vp6.eu
posta certificata: info@pec.vp6.eu