
Glamping · Esterno

Disegno indicativo, non in scala · posizioni da verificare sul posto

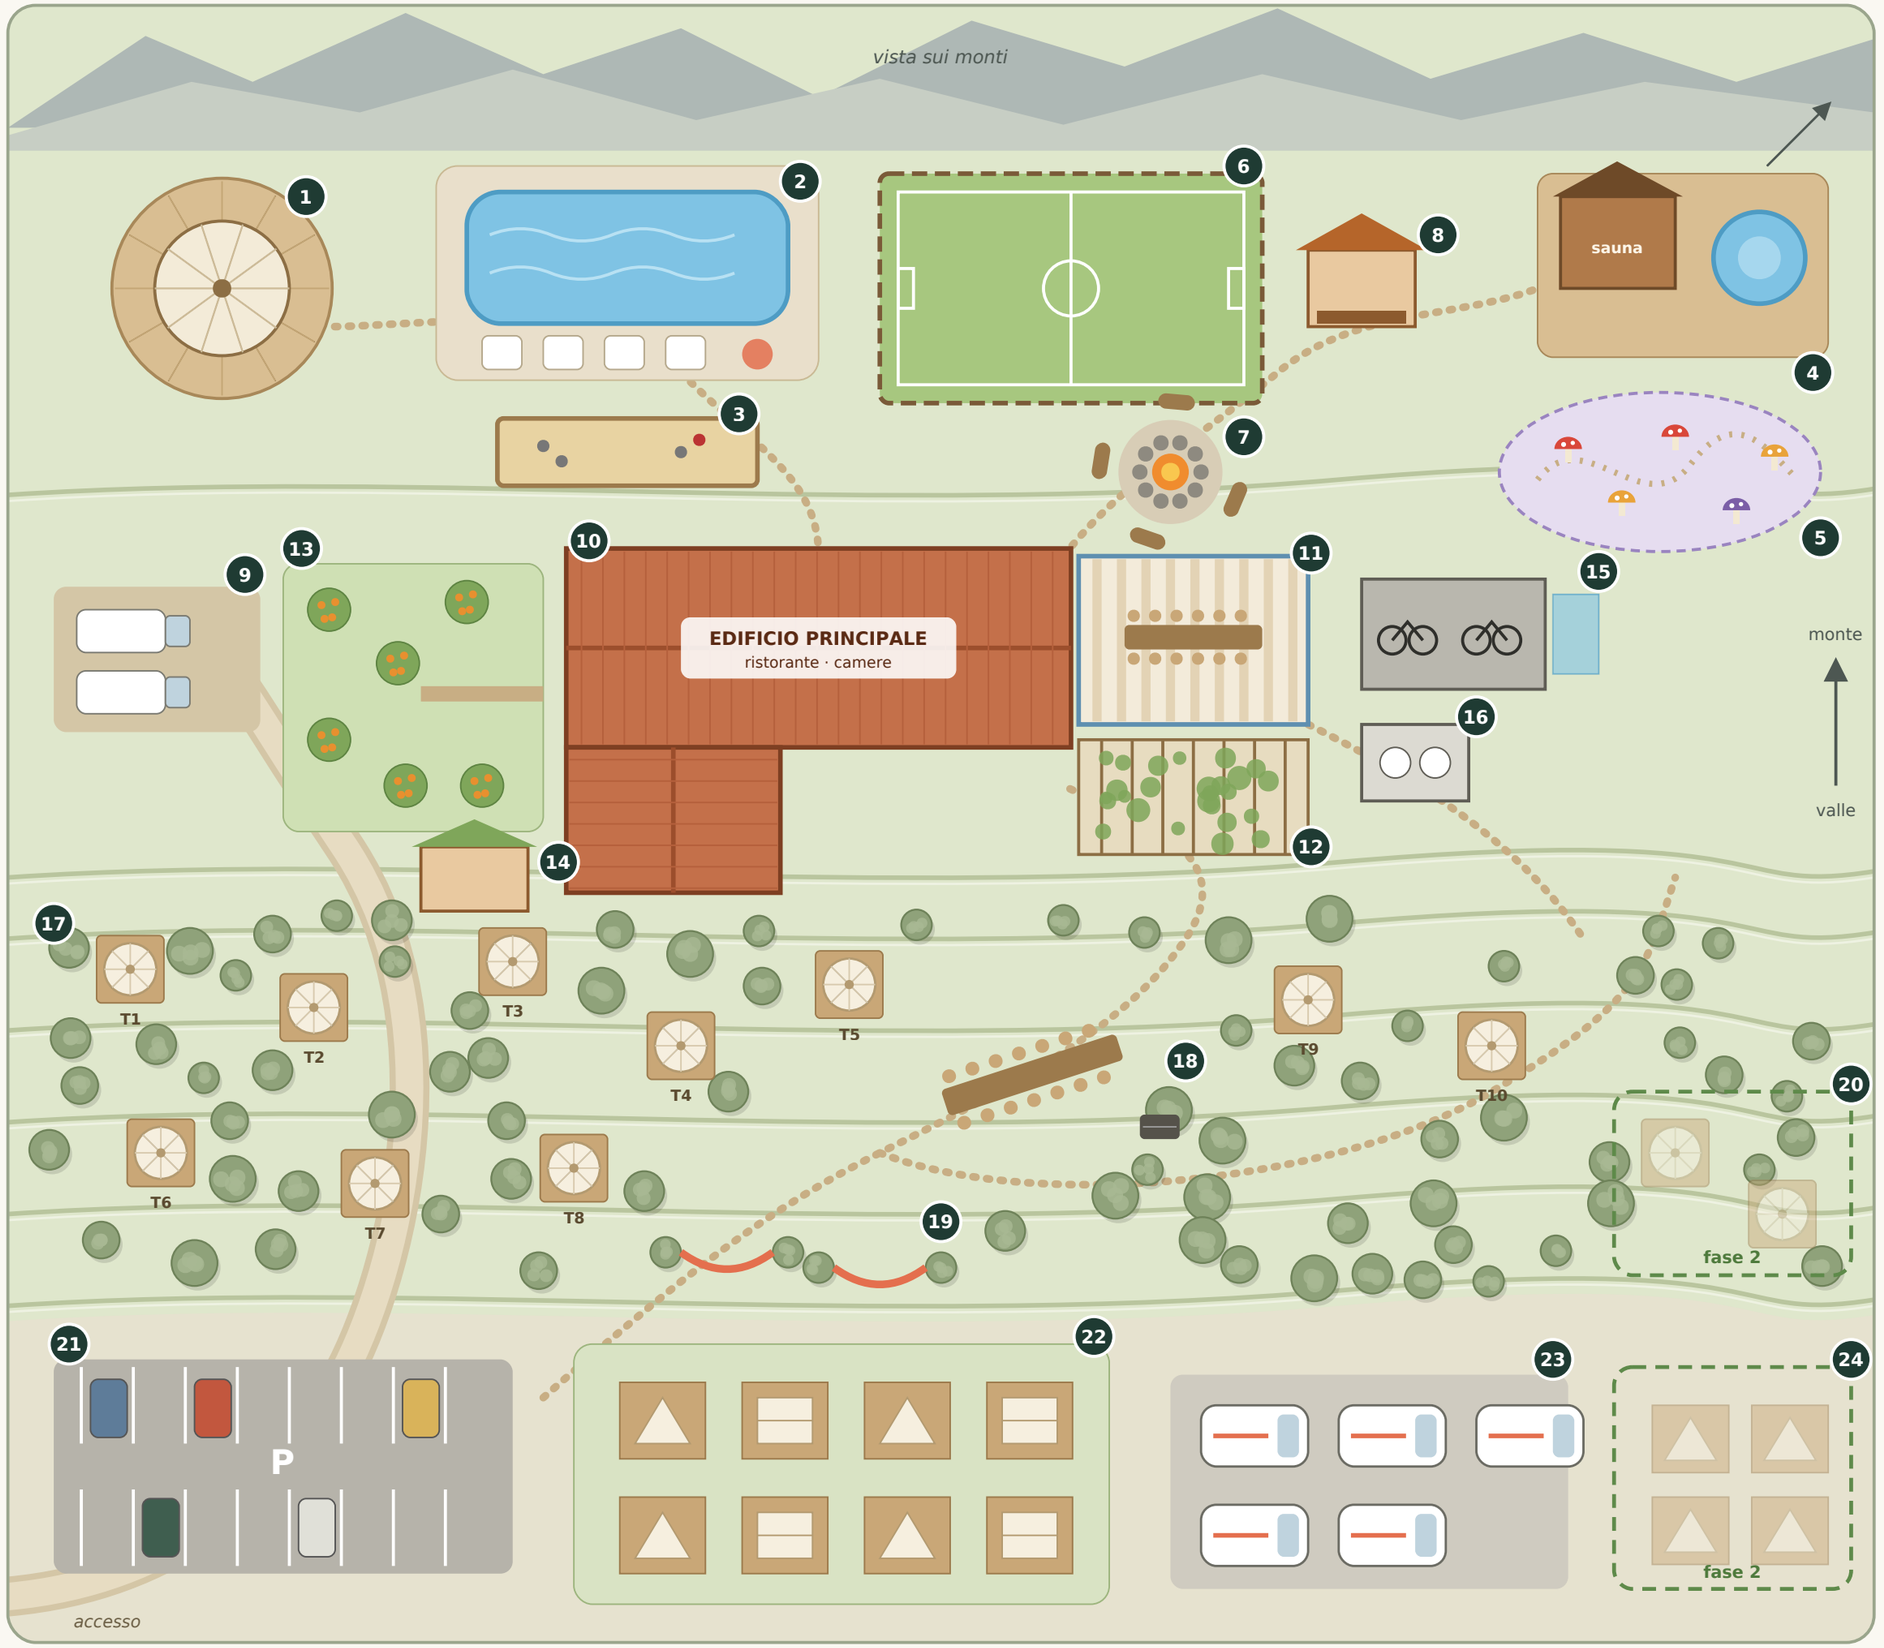

Legenda

ZONA ALTA

1. Yoga e meditazione · grande tipi
2. Piscina
3. Campo da pétanque
4. Sauna e jacuzzi panoramiche
5. Wonderland · parco fiabesco
6. Campo bike polo
7. Chill-out con fuoco
8. Bar esterno

EDIFICIO E GIARDINO

9. Sosta furgoni e clienti
10. Edificio principale
11. Sala esterna coperta
12. Pergolato aperitivo
13. Ingresso dal giardino
14. Negozietto esterno
15. Bike garage e bike wash
16. Lavanderia

ULIVETI TERRAZZATI

17. Glamping fase 1 · tende T1–T10
18. Tavolo lungo e barbecue
19. Amache
20. Altre tende · fase 2

ZONA BASSA

21. Parcheggio glamping
22. Campeggio · piattaforme
23. Zona camper
24. Campeggio · fase 2

Bordo tratteggiato = fase 2


Sentieri interni

Biliardo: posizione da indicare


Glamping · Interno edificio

Disegno indicativo, non in scala · disposizione da verificare con le misure reali

PIANO RISTORANTE

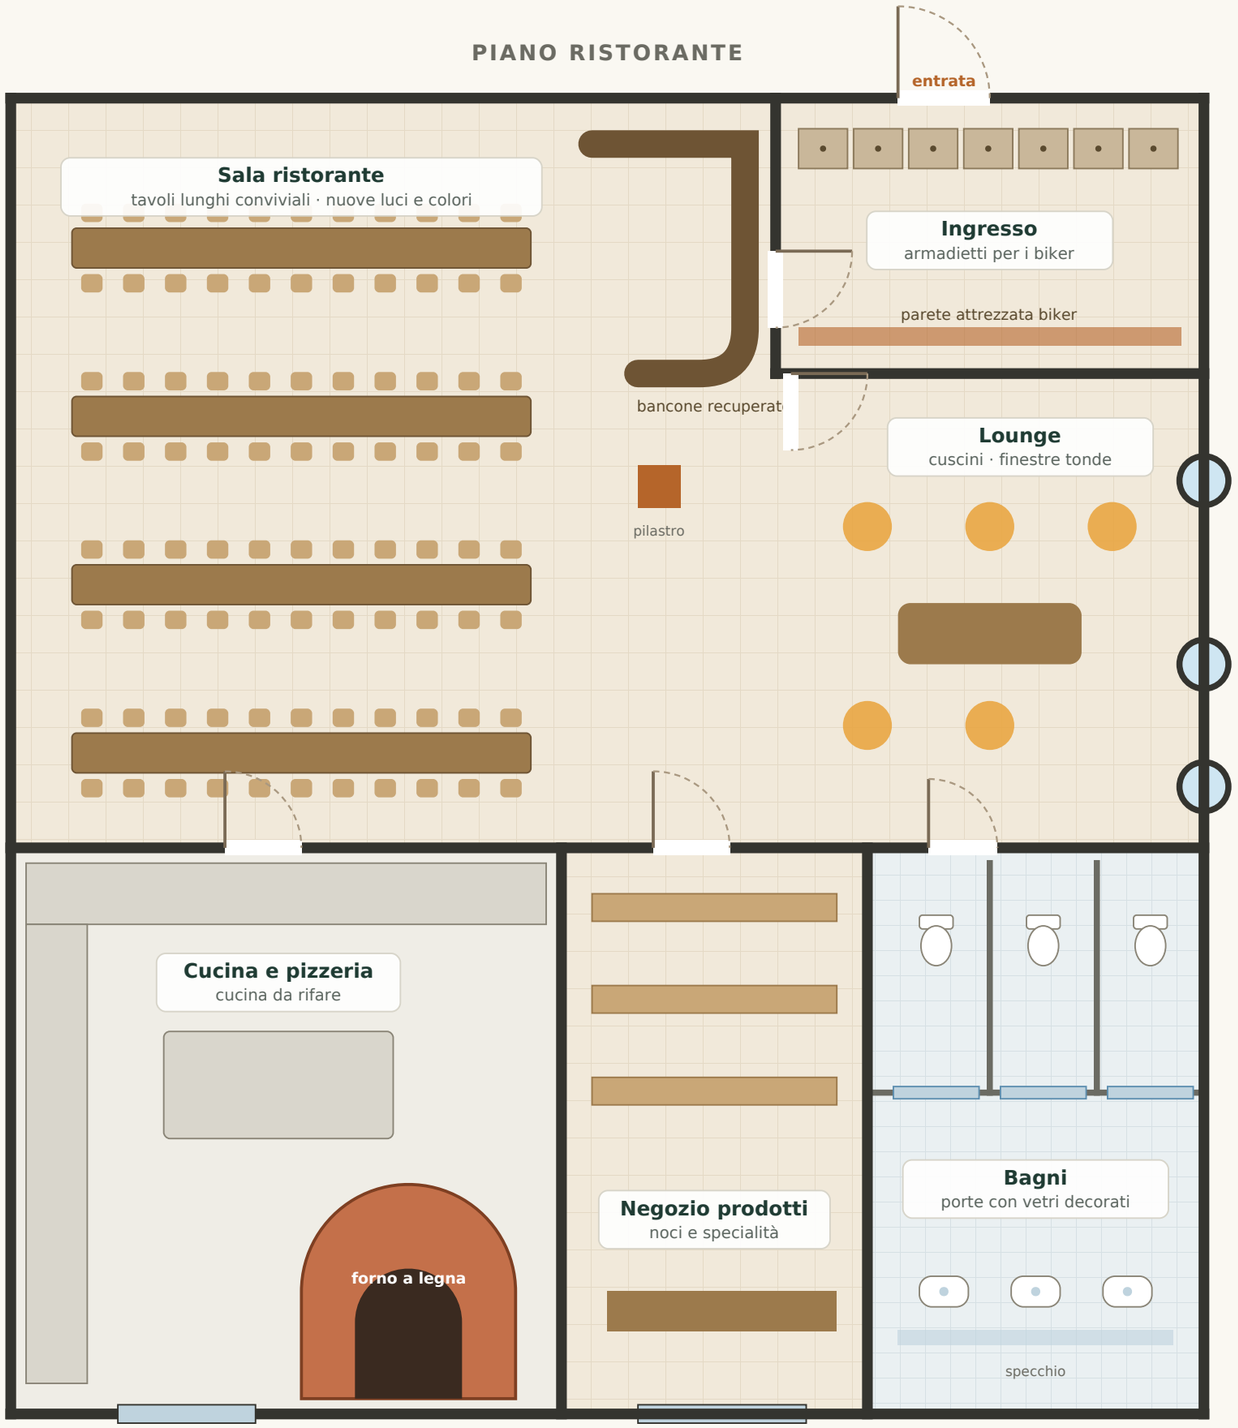

CAMERE E TRILOCALE

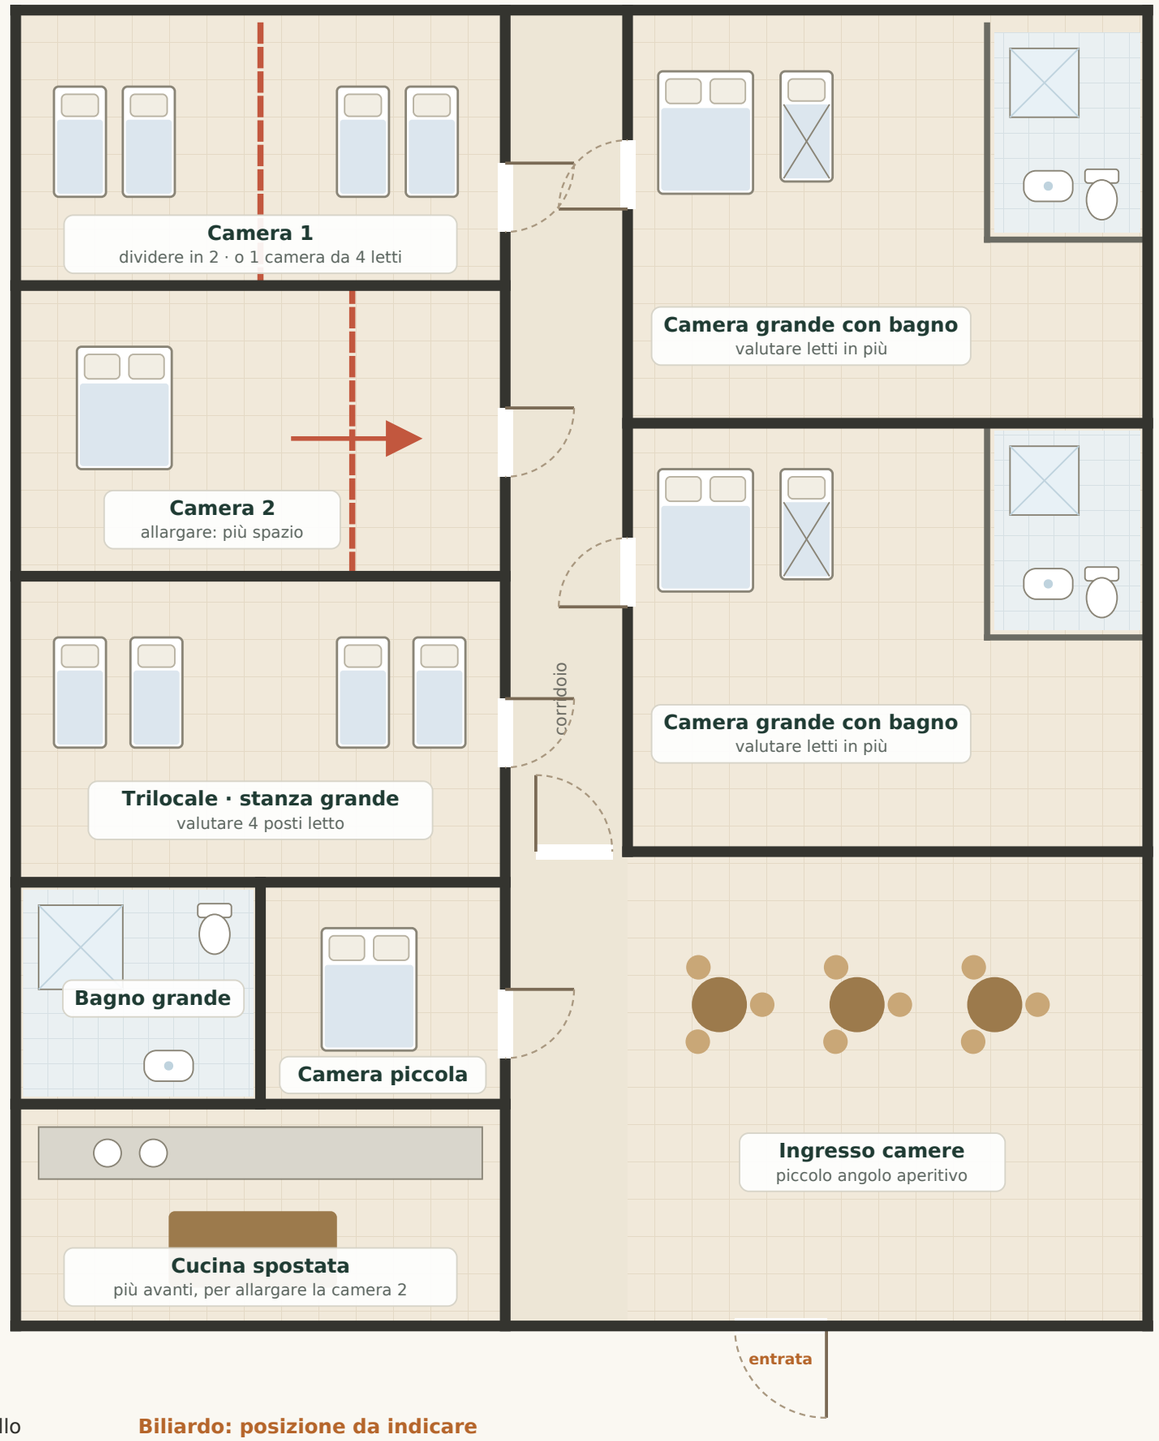

Muro nuovo o da spostare

Letto singolo

Letto matrimoniale

Letto a castello

Biliardo: posizione da indicare