Glamping – tutte le prove di design

Disegni, prove 3D e proposta attuale

Piano terra · Camere · Esterno


Ottobre 2026 · Immagini indicative, misure da verificare sul posto

1 · Disegni iniziali

1 · DISEGNI INIZIALI

Schizzo originale

Il vostro schizzo a mano del piano terra (dal business plan).

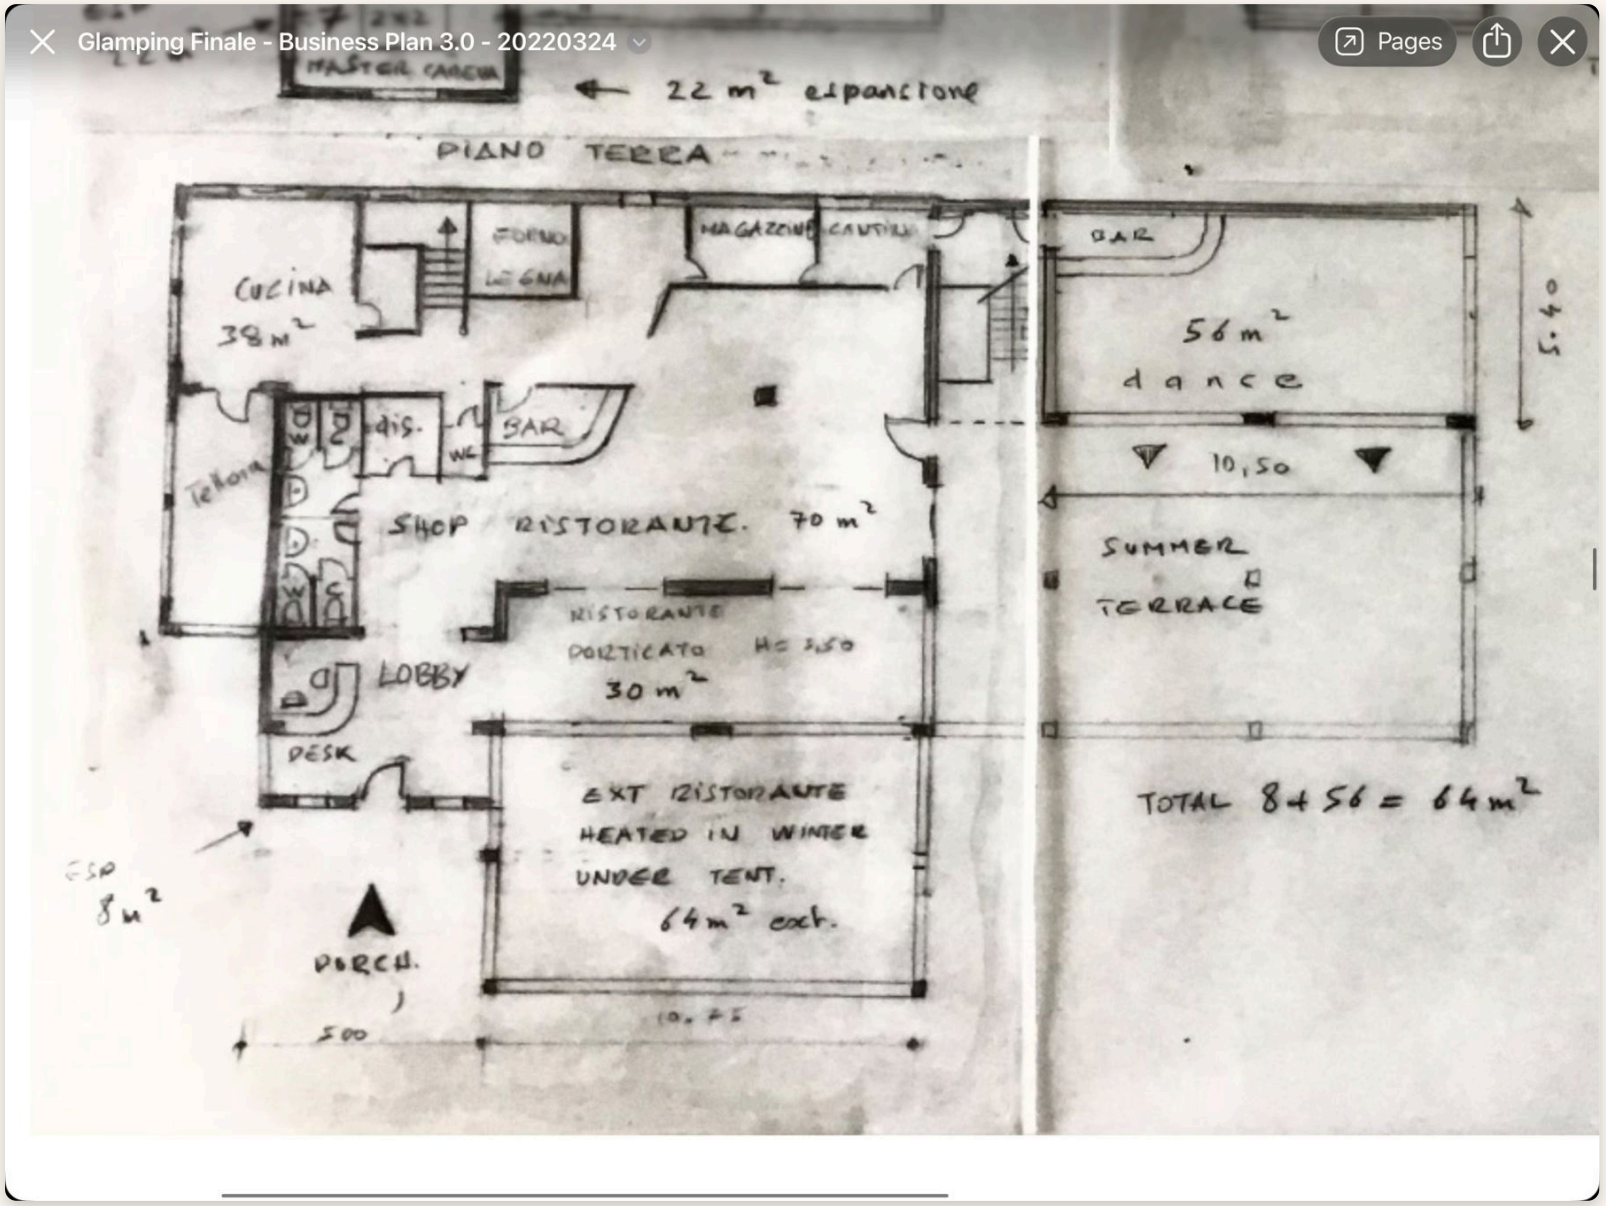


1 · DISEGNI INIZIALI

Bancone self-service

Prima idea: bancone lungo davanti al muro di magazzino e cantina, il vecchio bar tolto.

Piano terra – proposta bancone self-service + cassa

Schema indicativo ricavato dallo schizzo (scala ≈ 1:100, misure da verificare in loco). Nessun muro demolito.

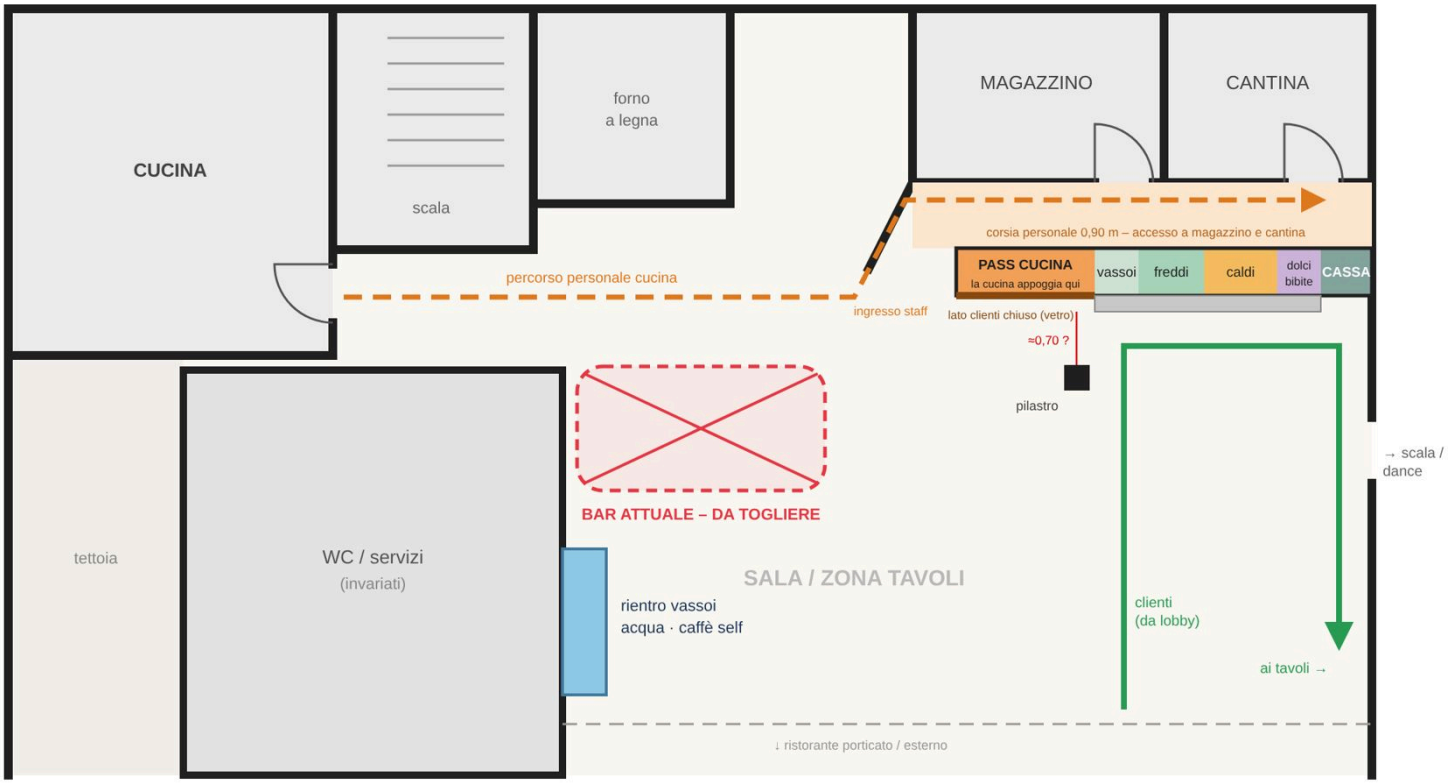

Come funziona

1. Bancone lungo ≈ 5,70 m davanti al muro di magazzino/cantina, staccato di 0,90 m: il muro resta intatto e le porte si usano dalla corsia.
2. Il personale esce dalla cucina, entra nella corsia dal lato sinistro e appoggia i piatti sul PASS (chiuso verso i clienti) e sui banchi.
3. Il cliente parte dal pilastro: vassoio → freddi → caldi → dolci/bibite → cassa, poi va ai tavoli. Flussi di staff e clienti non si incrociano.
4. Dove c'era il bar: rientro vassoi sporchi (vicino alla cucina) + punto acqua/caffè self.

⚠ Da misurare: distanza muro–pilastro. Se è sotto ~3,10 m, davanti al pilastro non c'è spazio per la coda: per questo lì c'è il PASS e la fila parte dopo.


1 · DISEGNI INIZIALI

Bar moderno con cassa al centro

Ritiro · vetrina pizze · cassa · birre, con la parete «Good Food».


Bar moderno “Good Food” – cassa al centro, ritiro e birre ai lati

Pianta schematica dallo schizzo (≈ 1:100, misure da verificare). Nessun muro demolito.

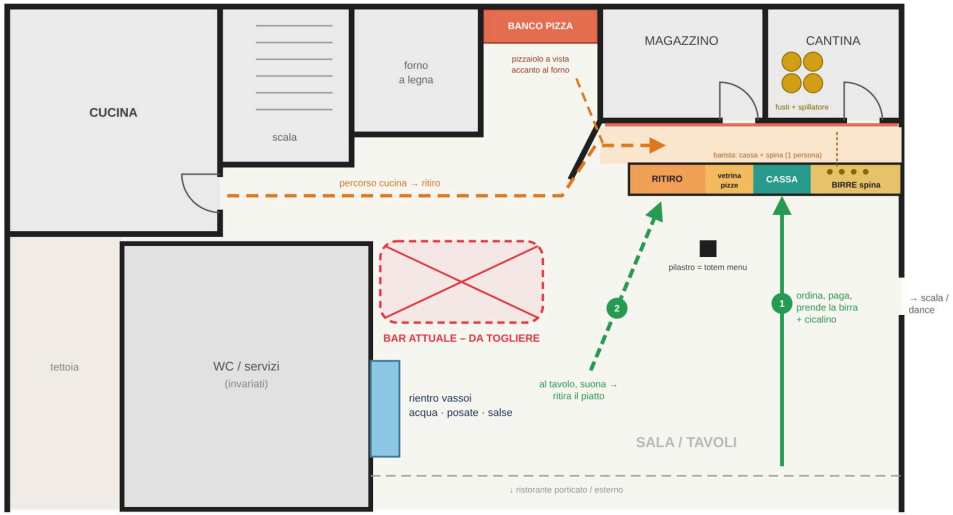

Vista frontale del bar (dalla sala)

Parete magazzino/cantina come parete grafica: porte rasomuro mimetizzate, insegna luminosa, schermi menu sopra la cassa.

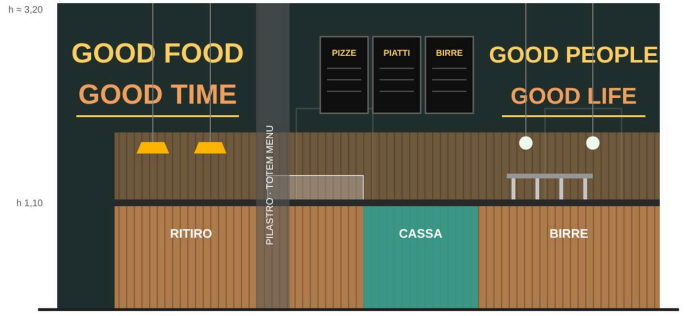

Perché così

- Cassa al centro: un solo barista fa cassa e spina, e in due passi aiuta anche al ritiro. La fila va dritta verso la sala, il pilastro non dà fastidio.
- Ritiro a sinistra, vicino all'ingresso della cucina e al forno: cucina e pizzaiolo fanno 1–2 metri per appoggiare i piatti.
- Birre a destra, attaccate alla cantina: fusti in cantina e linee corte fino alle spine (solo un piccolo foro, nessun muro rotto).
- Fast food “ordina e paga → cicalino → ritira”: niente fila lunga col vassoio lungo il bancone, più veloce nelle ore di punta.
- Parete dietro tutta grafica: GOOD FOOD · GOOD TIME · GOOD PEOPLE · GOOD LIFE, con porte rasomuro e luce calda.

⚠ Da verificare in loco: dove esce la bocca del forno, altezza soffitto, distanza muro–pilastro, passaggio linee birra cantina → bancone.

1 · DISEGNI INIZIALI

Tre varianti di colore del bar

A Notte industrial · B Natura glamping · C Sunset pop.

Bar “Good Food” – 3 varianti di colore


Vista frontale dalla sala. Stessa disposizione: ritiro · vetrina pizze · cassa · birre. Larghezza parete ≈ 6,30 m, bancone h 1,10 m.



A · Notte industrial

Parete antracite-verde scuro, scritte neon caldo. Fronte bancone in listelli di rovere scuro, piano nero opaco, lampade industriali nere. Effetto pub/birreria moderna, bello la sera.


parete	neon	rovere	cassa
#22302e	#ffd166	#8a5d36	#2a9d8f

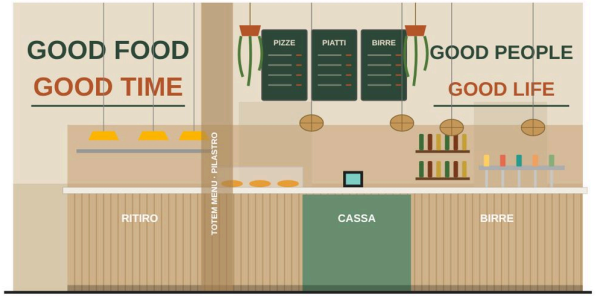

B · Natura glamping

Parete chiara color sabbia (calce/resina), scritte verde bosco e ruggine, legno naturale chiaro, lampade in rattan e piante pendenti. Luminoso, caldo, in linea con il glamping.

parete	verde bosco	ruggine	legno
#eadfcb	#2f4a3a	#b5562b	#d2b48c

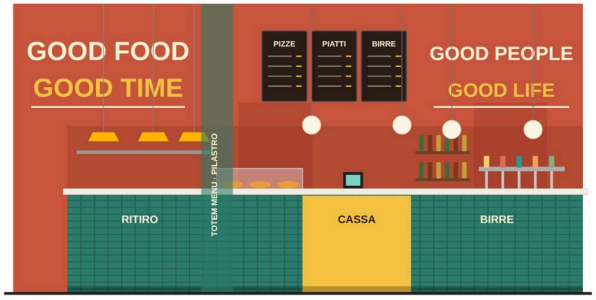

C · Sunset pop

Parete terracotta, scritte crema e senape, fronte bancone in piastrelle verdi lucide, lampade a sfera opaline. Allegro e fotogenico: perfetto per le foto social dei clienti.

terracotta	crema	senape	verde
#c8553d	#fff3d6	#f6c445	#2f7d6d

Dettagli comuni: lampade scaldavivande sul ritiro, vetrina pizze, POS, 5 spine con colonna, mensola bottiglie, porte rasomuro verniciate come la parete. Il pilastro davanti al bancone si riveste (metallo / legno / piastrelle secondo la variante) e diventa totem con menu e QR code.

1 · DISEGNI INIZIALI

Pianta completa del ristorante

Tutti i tavoli e i posti a sedere (circa 96).

Ristorante completo – piano terra, proposta di arredo

Schema dallo schizzo (≈ 1:300, misure da verificare). Self-service “ordina, paga, ritira”. Numeri = posti a sedere.



- Percorso clienti: porch → lobby → porticato → sala → cassa (ordina, paga, birra, cicalino)
- Percorso personale: cucina e forno → ritiro (non incrocia i clienti)
- Stazione self vicino ai WC: posate, acqua, salse e rientro vassoi sporchi verso la cucina

Totale ≈ 96 posti a tavola + ~20 in terrazza lounge

- Sala: tavolo sociale da 12 (Good People), tavolini da 2 e da 4, mensola con sgabelli per la birra veloce vicino alle spine.
- Porticato = lounge chill-out: pianoforte, camino, divanetti e tavolini h 70 per mangiare comodi. Vetrate + tende.
- Esterno sotto tenda: 8 tavoloni da 6 in legno (famiglie e gruppi del glamping), riscaldatori nel corridoio centrale.
- Il corridoio tra cucina e ritiro resta libero da tavoli. Arredi mobili: si possono unire i tavoli per gruppi ed eventi.


1 · DISEGNI INIZIALI

Porticato come lounge

Lounge chill-out con piano bar e camino.

Porticato → Lounge bar chill-out con piano bar e camino

Pianta di dettaglio (≈ 1:70, misure da verificare). Chiuso con vetrate d'inverno, aperto d'estate. Si mangia comodi sui divanetti.

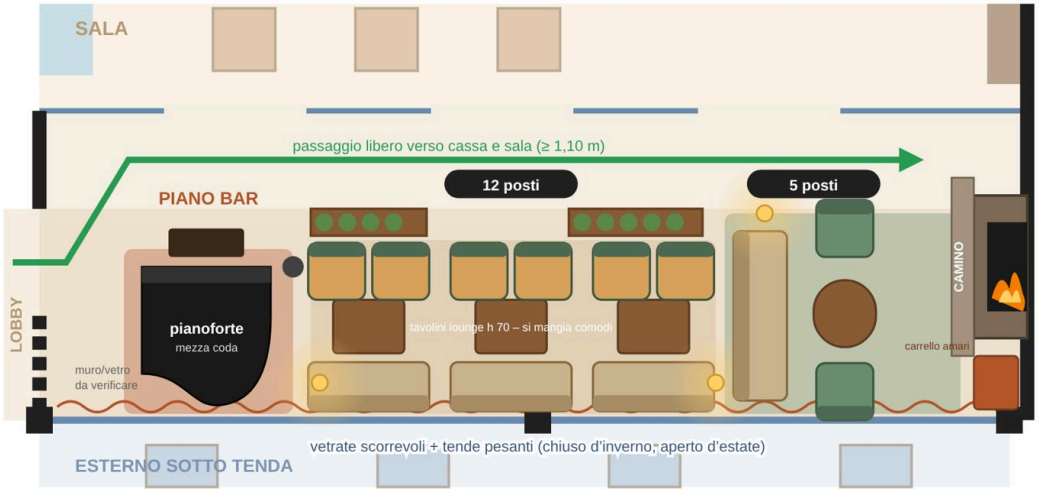

Parete del camino (vista frontale)



Pietra al centro, scritta luminosa GOOD LIFE sopra la mensola, nicchie per la legna ai lati, panca in legno con cuscini.

Atmosfera

- luce calda dimmerabile (2700 K), lampade da terra, niente luci forti
- tappeti, tende pesanti e pannelli in feltro: assorbono il rumore
- piano bar dal vivo a volume basso, sound diffuso anche in sala

Mangiare in lounge

- tavolini h 70 cm con divanetti e poltroncine: si cena comodi
- stesso self-service: ordina in cassa, il cicalino suona, ritira
- la sera servizio al tavolo per drink, cocktail e amari (+ scontrino medio)

Camino – da verificare

- a legna: serve canna fumaria e pratica con i Vigili del Fuoco
- alternativa senza canna: bioetanolo o elettrico effetto fiamma 3D
- tenere 1 m libero davanti al fuoco, panca in pietra/legno ignifugo

Lounge ≈ 17 posti + piano · Totale ristorante ≈ 96 posti a tavola + terrazza lounge

Il pianoforte sta vicino all'ingresso dalla lobby: chi entra sente subito la musica. Il camino in fondo è il punto più tranquillo e intimo.


1 · DISEGNI INIZIALI

Piano terra low budget

Con le vostre idee: bar blu, bagni graffiti, murales, mobili recuperati.

Piano terra – versione “low budget” con le vostre idee

Colori, murales, adesivi e mobili recuperati (Props) + bar nuovo lungo il muro magazzino/cantina. Schema ≈ 1:250, misure da verificare.

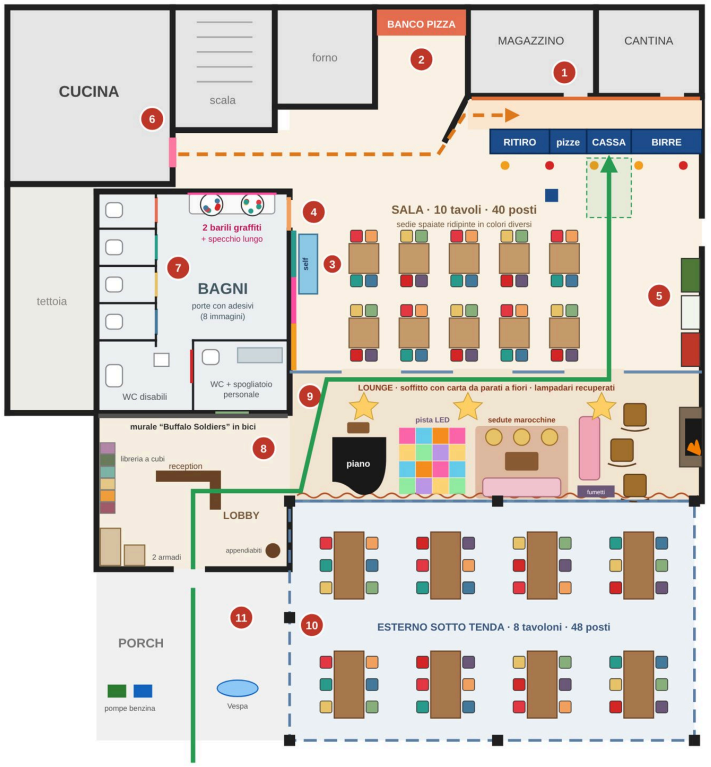

Legenda


1. **Bar blu nuovo:** lungo il muro magazzino/cantina: ritiro · pizze · cassa · birre. Bancone blu cannettato, parete dipinta ad archi, tende in velluto davanti alle porte, lampade arancio e rosse.
2. **Banco pizza:** a vista vicino al forno, a 1 m dal ritiro.
3. **Stazione self:** posate, acqua, salse e rientro vassoi (dove c’era il vecchio bar).
4. **Murales sala:** sul muro dei bagni verso la sala (volti pop / pois, come nelle vostre prove).
5. **3 mobili colorati:** verde, bianco, rosso sul muro di destra: credenze per piatti, bicchieri e tovaglioli.
6. **Porta cucina rosa:** ridipinta, come nel vostro render.
7. **Bagni rifatti:** lavabo comune con 2 barili graffiti + specchio lungo con cornice graffiti; 4 WC + WC disabili + WC personale; porte con adesivi (8 immagini).
8. **Ingresso:** libreria a cubi colorata, 2 armadi, appendiabiti (Props 61), murale Buffalo Soldiers in bici.
9. **Lounge:** camino + 3 sedie a dondolo (Props 7), piano + sgabello (117), pista LED “Saturday Night Fever”, sedute marocchine e cuscini afghani (41), divano rosa (11), mobile fumetti.
10. **Esterno sotto tenda:** tavoloni in legno (anche tavolo falegname Props 6 e barella-tavolo 17), sedie colorate.
11. **Porch:** pompe di benzina (21), insegne Caltex (71), Vespa (67): angolo foto all’arrivo.

Bar blu e bagni graffiti

Vista frontale del bar blu e dei bagni con barili graffitati e porte con adesivi.

Il vostro bar blu sul muro nuovo + bagni graffiti

Stesso stile del vostro render (bancone blu cannettato, archi, velluto, lampade arancio/rosse), ma nella nuova posizione con ritiro · pizze · cassa · birre.

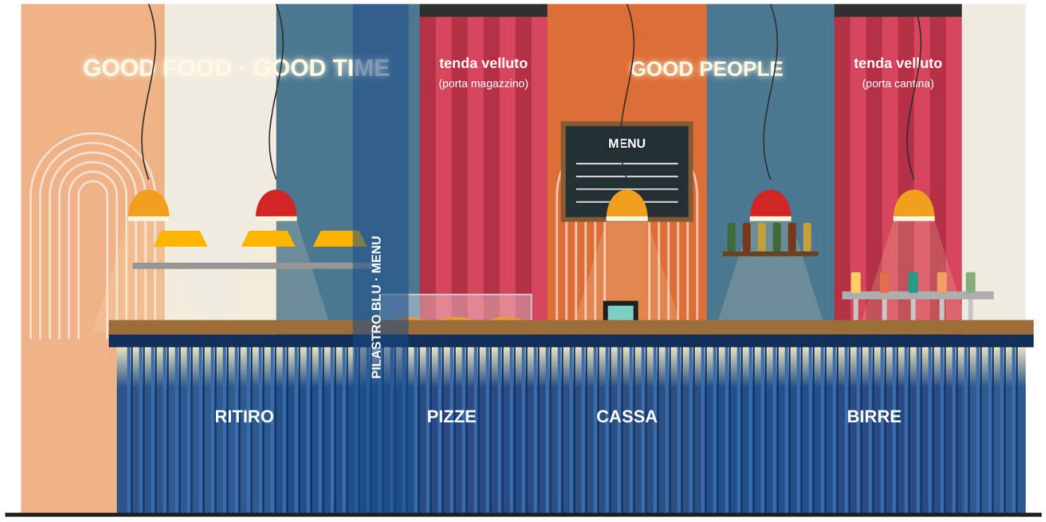


Bancone: struttura in legno/OSB, pannelli cannettati in MDF verniciati blu, top in legno, striscia LED sotto il piano.

Parete: archi dipinti a mano con nastro e vernice (fai da te).

Tende in velluto: coprono le porte di magazzino e cantina.

Lampade: 2 arancio + 3 rosse (o le lampade arancioni dei Props 14 e 24).

Bagni: lavabo comune con 2 barili graffiti + porte con adesivi

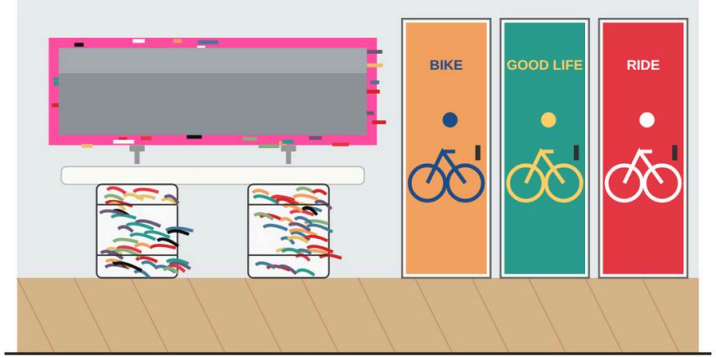

Barili: fusti in metallo da 200 L, puliti, fatti graffitare da uno street artist locale, finitura trasparente lavabile. Sopra: lavabo doppio in resina, rubinetti a muro.

Specchio lungo con cornice graffiti abbinata.

Porte: adesivo in vinile laminato (lavabile), 8 immagini = 4 WC + disabili + personale + ingresso bagni + porta cucina.
Usate immagini libere o con licenza, o fatele disegnare: le locandine famose hanno il copyright.

2 · Prove 3D

2 · PROVE 3D

Versione pop (troppo americana)

Prima prova 3D: colori pop, bancone blu, tende in velluto.









2 · PROVE 3D

Stile ligure classico (troppo pesante)

Pietra a vista, archi, travi scure, noce antico, ferro battuto.









2 · PROVE 3D

Stile ligure classico (troppo pesante) (continua)

Pietra a vista, archi, travi scure, noce antico, ferro battuto.



2 · PROVE 3D

Mix moderno e antico

Pareti bianche, poca pietra, bancone blu cannettato, sedie bistrot. Aperture quadrate.









2 · PROVE 3D

Mix moderno e antico (continua)

Pareti bianche, poca pietra, bancone blu cannettato, sedie bistrot. Aperture quadrate.



2 · PROVE 3D

Mix moderno e antico – con archi

La stessa versione con gli archi tra sala e lounge.









2 · PROVE 3D

Mix moderno e antico – con archi (continua)

La stessa versione con gli archi tra sala e lounge.



v4 · Leggero

Pareti bianche, sedie impagliate dipinte, tavolo lungo in ferro, murale Buffalo Soldiers.









2 · PROVE 3D

v4 · Leggero (continua)

Pareti bianche, sedie impagliate dipinte, tavolo lungo in ferro, murale Buffalo Soldiers.



2 · PROVE 3D

v5 · Officina industriale

Cemento, acciaio, pompe di benzina, flipper, insegna Caltex, Vespa.









2 · PROVE 3D

v5 · Officina industriale (continua)

Cemento, acciaio, pompe di benzina, flipper, insegna Caltex, Vespa.





2 · PROVE 3D

v7 · Casa ligure bianca

Bianco e legno, tovaglie di lino, sedie impagliate naturali, stufa.









2 · PROVE 3D

v7 · Casa ligure bianca (continua)

Bianco e legno, tovaglie di lino, sedie impagliate naturali, stufa.





v8 · Lounge aperta contemporanea

Tavoli lunghi condivisi, bancone in travertino, lanterne di carta, panca verde oliva.









2 · PROVE 3D

v8 · Lounge aperta contemporanea (continua)

Tavoli lunghi condivisi, bancone in travertino, lanterne di carta, panca verde oliva.






2 · PROVE 3D

v9 · Bar lungo con ribalta

Bancone da parete a parete (circa 8,7 m) con ribalta e passe per cucina e pizza.





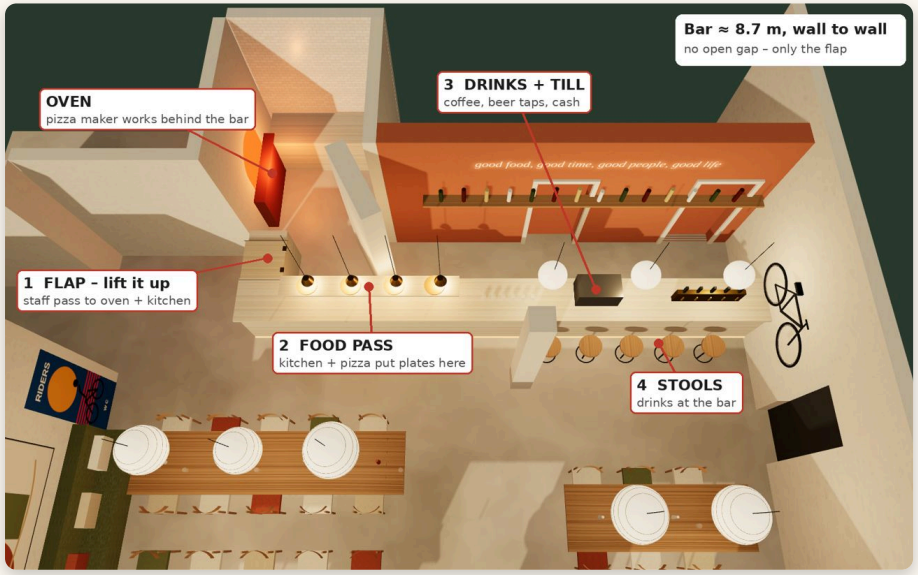



2 · PROVE 3D

v9 · Bar lungo con ribalta (continua)

Bancone da parete a parete (circa 8,7 m) con ribalta e passe per cucina e pizza.





2 · PROVE 3D

v10 · Foto Buffalo Soldiers e sedute a terra

La vostra foto originale all'ingresso, scaffali, lounge con sedute basse.









2 · PROVE 3D

v10 · Foto Buffalo Soldiers e sedute a terra (continua)

La vostra foto originale all'ingresso, scaffali, lounge con sedute basse.





2 · PROVE 3D

v11 · Ingresso con porte e armadietti

Le porte restano; scaffali per caschi, zaini e scarpe dei biker.









2 · PROVE 3D

v11 · Ingresso con porte e armadietti (continua)

Le porte restano; scaffali per caschi, zaini e scarpe dei biker.



2 · PROVE 3D

v12 · Piano terra ligure

Ritorno allo stile ligure: niente archi, poca pietra, tavoloni lunghi, parete gialla.









2 · PROVE 3D

v12 · Piano terra ligure (continua)

Ritorno allo stile ligure: niente archi, poca pietra, tavoloni lunghi, parete gialla.



2 · PROVE 3D

v13 · Ligure più moderno

Senza pietra, travi chiare, tavoli in rovere, grandi lampade in tessuto.









2 · PROVE 3D

v13 · Ligure più moderno (continua)

Senza pietra, travi chiare, tavoli in rovere, grandi lampade in tessuto.



2 · PROVE 3D

v14 · Lounge con cuscini Mah Jong

Grandi cuscini a terra in patchwork, stile Roche Bobois.





2 · PROVE 3D

v15 · Pianoforte, camino e piccola pista

Meno cuscini, pista in parquet, pianoforte vicino all'ingresso.





3 · Proposta attuale

3 · PROPOSTA ATTUALE

v16 · Pianoforte al camino e pista Saturday Night Fever

Pianoforte vicino al camino, pista a quadrati colorati luminosi, finestre ad arco, vetrate tra sala e lounge.









3 · PROPOSTA ATTUALE

Camere al piano superiore

Camera moderna con letto a scomparsa e camera italiana dipinta con i vostri mobili. Pavimento in legno.










3 · PROPOSTA ATTUALE

Colori della facciata

Giallo Liguria, rosso Portofino, arancio vivo, rosa Camogli.

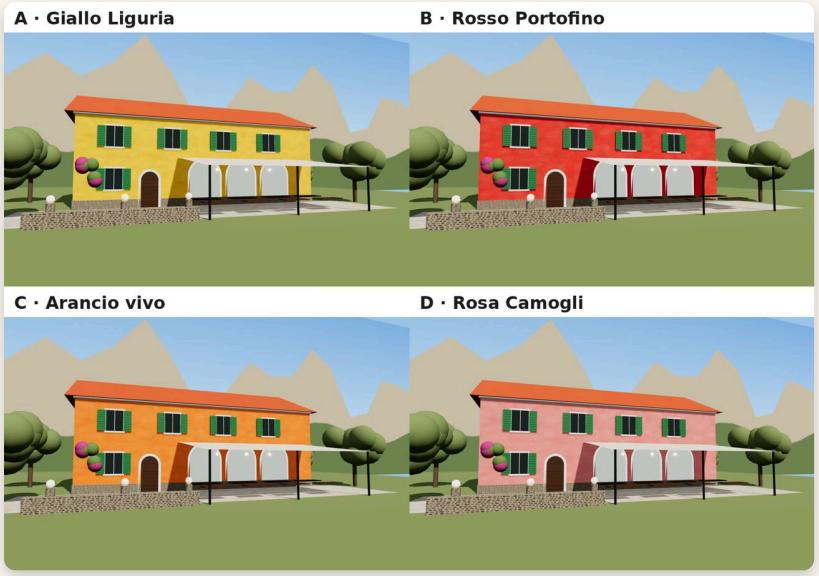







3 · PROPOSTA ATTUALE

Colori della facciata (continua)

Giallo Liguria, rosso Portofino, arancio vivo, rosa Camogli.

